Work scope

13-0969-PW-PE16-400 to F13-PP-401

Exported Oct 17, 2026 from Project Library. Route lines highlighted in their fluid colours.

Lines on the route

🟦	1.	**13-0969-PW-PE16-400**	PW	2000-F24-PID-PR-10019
🟦	2.	**13-0055-PW-SS2-400**	PW	2000-F24-PID-PR-10019
🟦	3.	**13-0055-PW-SS2-400**	PW	2000-F13-PID-PR-10002
🟫	4.	**1200-MECH-CERAMIC**	MECH	2000-F13-PID-PR-10002

Sheets

1.	**2000-F24-PID-PR-10019**	Rev MS_1	Process water, sheet 3
2.	**2000-F13-PID-PR-10002**	Rev MS_1	SAG and ball milling, sheet 1, Stage 1

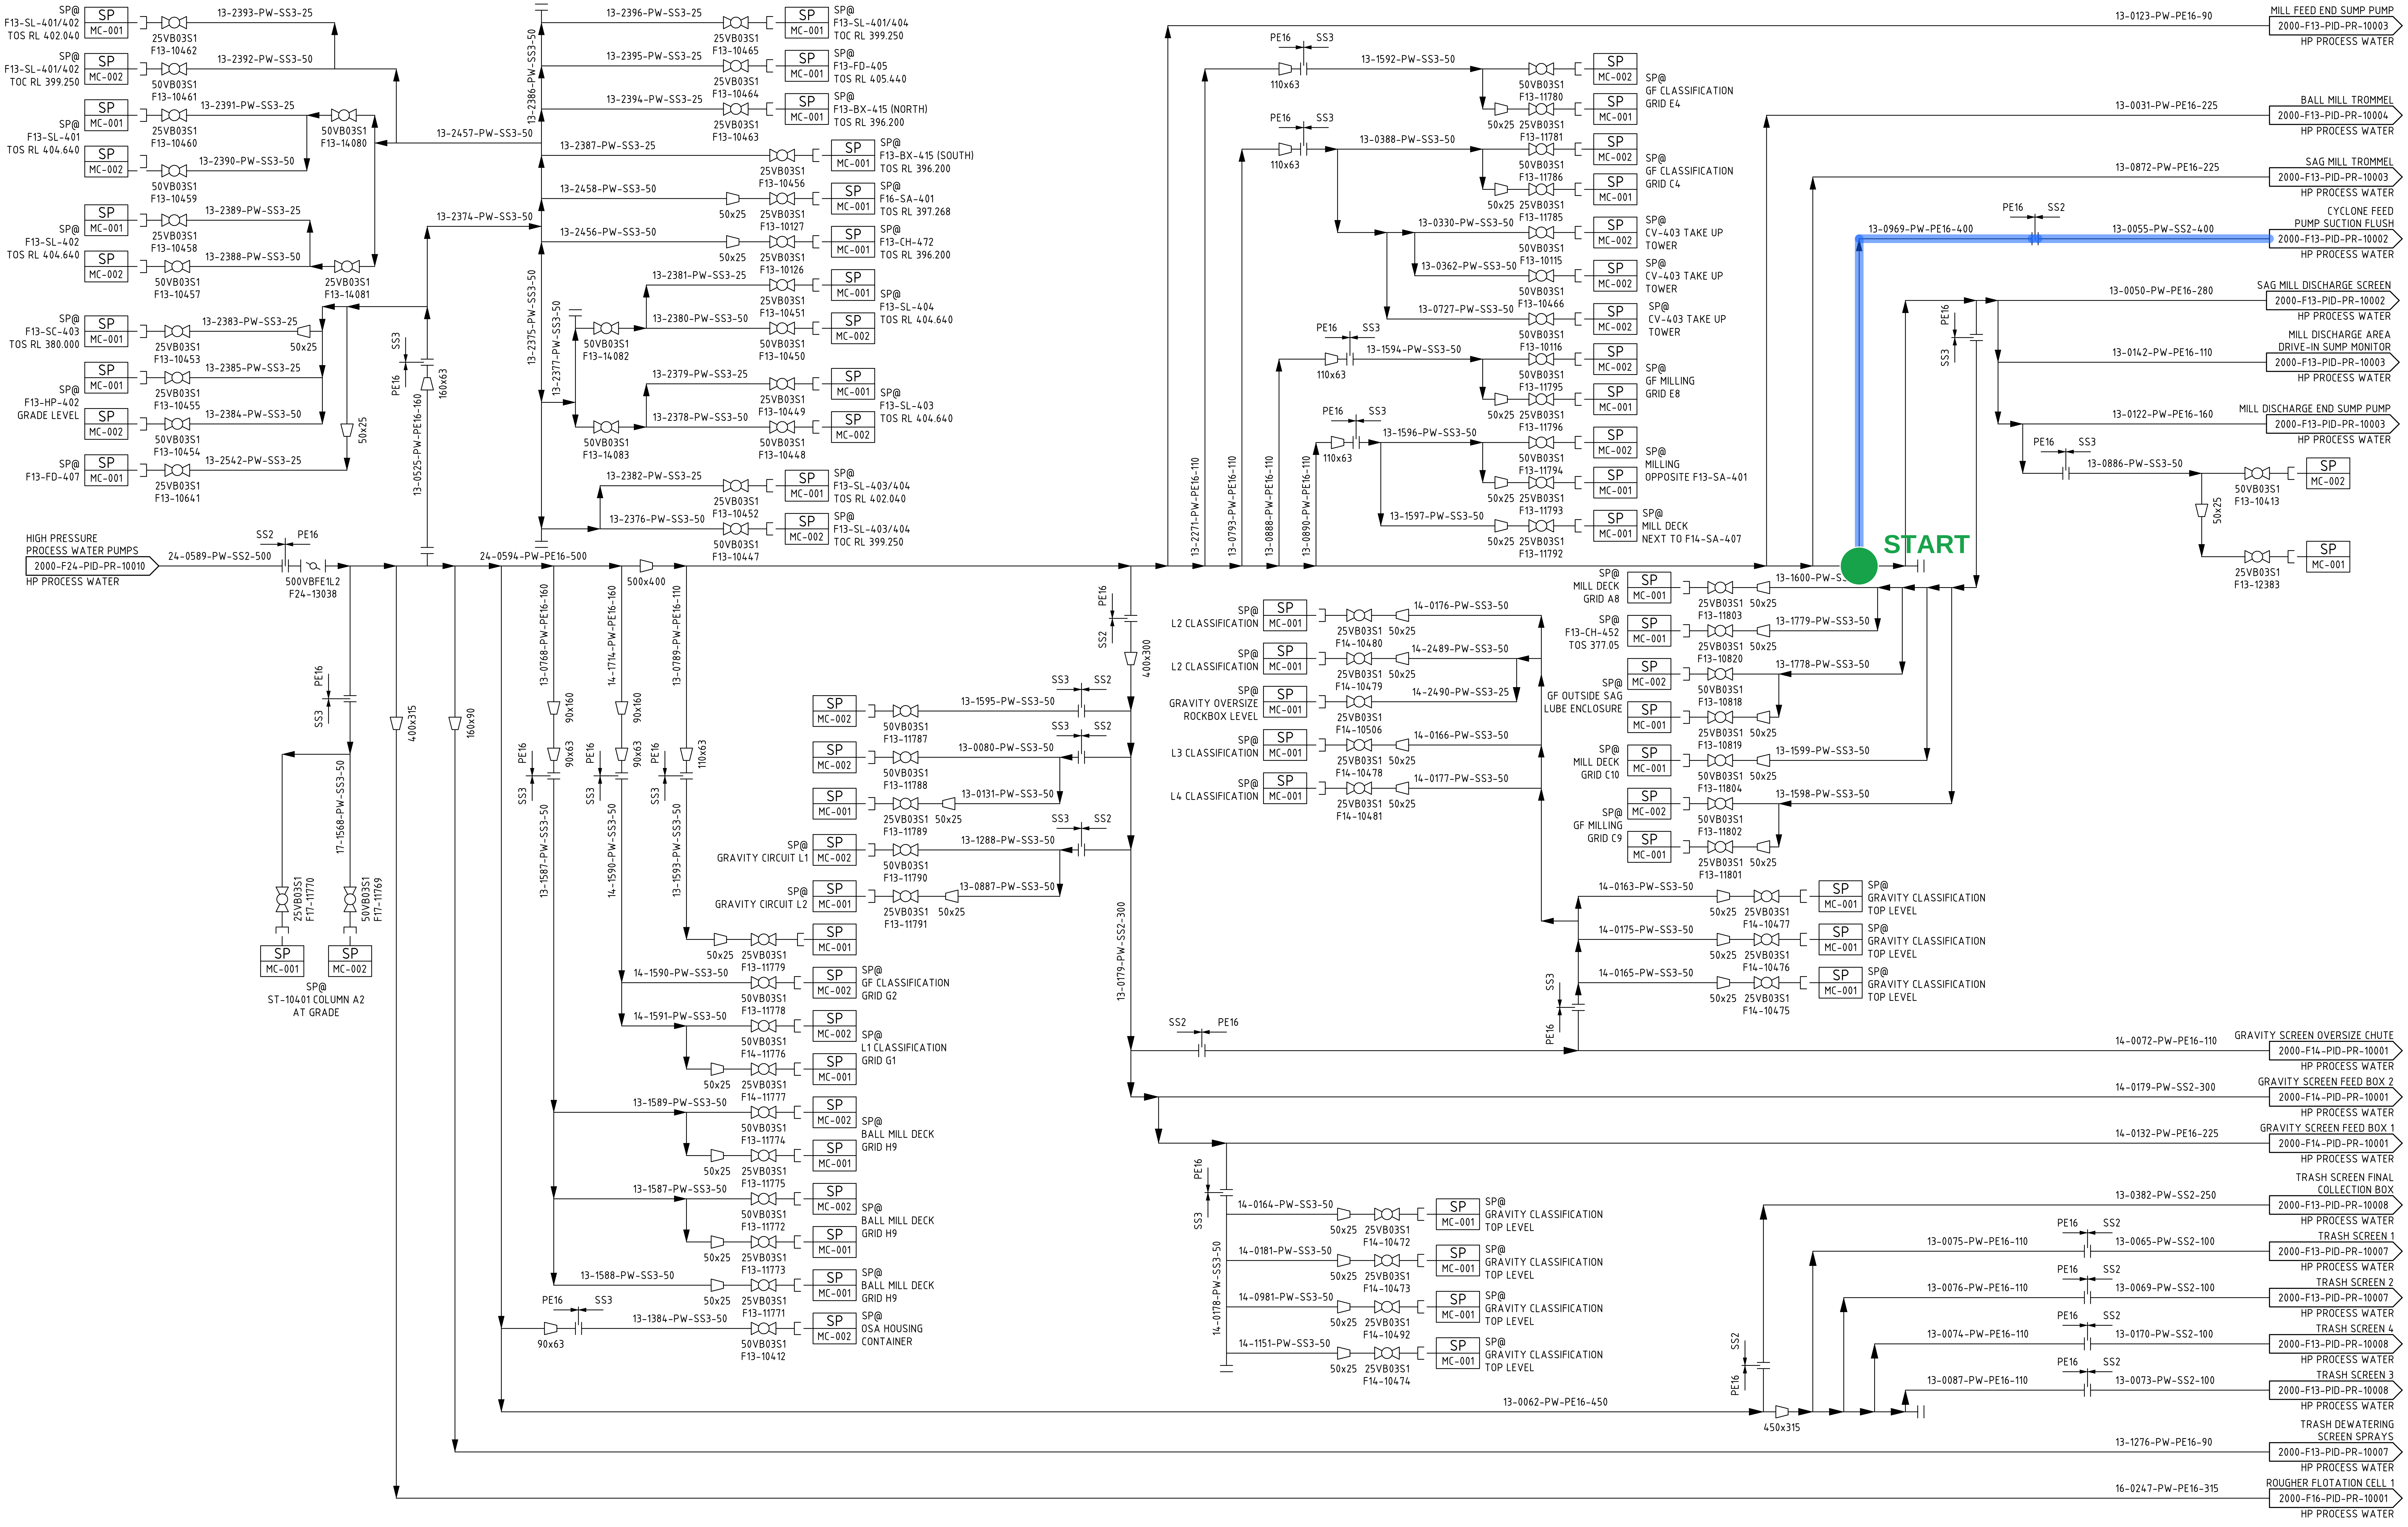
START
HIGH PRESSURE
PROCESS WATER PUMPS
2000-F24-PID-PR-10010
HP PROCESS WATER
24-0589-PW-SS2-500
SS2
PE16
500VBFE1L2
F24-13038
24-0594-PW-PE16-500
500x400
SP@
F13-SL-401/402
TOS RL 402.040
SP MC-001
25VB03S1
F13-10462
13-2393-PW-SS3-25
SP@
F13-SL-401/402
TOC RL 399.250
SP MC-002
50VB03S1
F13-10461
13-2392-PW-SS3-50
SP@
F13-SL-401
TOS RL 404.640
SP MC-001
25VB03S1
F13-10460
13-2391-PW-SS3-25
50VB03S1
F13-14080
SP MC-002
50VB03S1
F13-10459
13-2390-PW-SS3-50
13-2457-PW-SS3-50
SP@
F13-SL-402
TOS RL 404.640
SP MC-001
25VB03S1
F13-10458
13-2389-PW-SS3-25
SP MC-002
50VB03S1
F13-10457
13-2388-PW-SS3-50
25VB03S1
F13-14081
13-2374-PW-SS3-50
SP@
F13-SC-403
TOS RL 380.000
SP MC-001
25VB03S1
F13-10453
13-2383-PW-SS3-25
50x25
SP@
F13-HP-402
GRADE LEVEL
SP MC-001
25VB03S1
F13-10455
13-2385-PW-SS3-25
SP MC-002
50VB03S1
F13-10454
13-2384-PW-SS3-50
50x25
SP@
F13-FD-407
SP MC-001
25VB03S1
F13-10641
13-2542-PW-SS3-25
SS3
PE16
160x63
13-0525-PW-PE16-160
PE16
SS3
17-1568-PW-SS3-50
25VB03S1
F17-11770
50VB03S1
F17-11769
SP MC-001
SP MC-002
SP@
ST-10401 COLUMN A2
AT GRADE
400x315
160x90
13-2386-PW-SS3-50
13-2375-PW-SS3-50
13-2377-PW-SS3-50
13-2396-PW-SS3-25
25VB03S1
F13-10465
SP MC-001
SP@
F13-SL-401/404
TOC RL 399.250
13-2395-PW-SS3-25
25VB03S1
F13-10464
SP MC-001
SP@
F13-FD-405
TOS RL 405.440
13-2394-PW-SS3-25
25VB03S1
F13-10463
SP MC-001
SP@
F13-BX-415 (NORTH)
TOS RL 396.200
13-2387-PW-SS3-25
25VB03S1
F13-10456
SP MC-001
SP@
F13-BX-415 (SOUTH)
TOS RL 396.200
13-2458-PW-SS3-50
50x25
25VB03S1
F13-10127
SP MC-001
SP@
F16-SA-401
TOS RL 397.268
13-2456-PW-SS3-50
50x25
25VB03S1
F13-10126
SP MC-001
SP@
F13-CH-472
TOS RL 396.200
13-2381-PW-SS3-25
25VB03S1
F13-10451
SP MC-001
SP@
F13-SL-404
TOS RL 404.640
50VB03S1
F13-14082
13-2380-PW-SS3-50
50VB03S1
F13-10450
SP MC-002
13-2379-PW-SS3-25
25VB03S1
F13-10449
SP MC-001
SP@
F13-SL-403
TOS RL 404.640
50VB03S1
F13-14083
13-2378-PW-SS3-50
50VB03S1
F13-10448
SP MC-002
13-2382-PW-SS3-25
25VB03S1
F13-10452
SP MC-001
SP@
F13-SL-403/404
TOS RL 402.040
13-2376-PW-SS3-50
50VB03S1
F13-10447
SP MC-002
SP@
F13-SL-403/404
TOC RL 399.250
13-0768-PW-PE16-160
90x160
PE16
SS3
90x63
13-1587-PW-SS3-50
14-1714-PW-PE16-160
90x160
PE16
SS3
90x63
14-1590-PW-SS3-50
13-0789-PW-PE16-110
PE16
SS3
110x63
13-1593-PW-SS3-50
50x25
25VB03S1
F13-11779
SP MC-001
14-1590-PW-SS3-50
50VB03S1
F13-11778
SP MC-002
SP@
GF CLASSIFICATION
GRID G2
14-1591-PW-SS3-50
50VB03S1
F14-11776
SP MC-002
SP@
L1 CLASSIFICATION
GRID G1
50x25
25VB03S1
F14-11777
SP MC-001
13-1589-PW-SS3-50
50VB03S1
F13-11774
SP MC-002
SP@
BALL MILL DECK
GRID H9
50x25
25VB03S1
F13-11775
SP MC-001
13-1587-PW-SS3-50
50VB03S1
F13-11772
SP MC-002
SP@
BALL MILL DECK
GRID H9
50x25
25VB03S1
F13-11773
SP MC-001
13-1588-PW-SS3-50
50x25
25VB03S1
F13-11771
SP MC-001
SP@
BALL MILL DECK
GRID H9
PE16
SS3
90x63
13-1384-PW-SS3-50
50VB03S1
F13-10412
SP MC-002
SP@
OSA HOUSING
CONTAINER
SP MC-002
50VB03S1
F13-11787
13-1595-PW-SS3-50
SS3
SS2
SP MC-002
50VB03S1
F13-11788
13-0080-PW-SS3-50
SS3
SS2
SP MC-001
25VB03S1
F13-11789
50x25
13-0131-PW-SS3-50
SP@
GRAVITY CIRCUIT L1
SP MC-002
50VB03S1
F13-11790
13-1288-PW-SS3-50
SS3
SS2
SP@
GRAVITY CIRCUIT L2
SP MC-001
25VB03S1
F13-11791
50x25
13-0887-PW-SS3-50
PE16
SS3
400x300
13-0179-PW-SS2-300
SS2
PE16
13-2271-PW-PE16-110
13-0793-PW-PE16-110
13-0888-PW-PE16-110
13-0890-PW-PE16-110
PE16
SS3
110x63
13-1592-PW-SS3-50
50VB03S1
F13-11780
SP MC-002
SP@
GF CLASSIFICATION
GRID E4
50x25
25VB03S1
F13-11781
SP MC-001
PE16
SS3
110x63
13-0388-PW-SS3-50
50VB03S1
F13-11786
SP MC-002
SP@
GF CLASSIFICATION
GRID C4
50x25
25VB03S1
F13-11785
SP MC-001
13-0330-PW-SS3-50
50VB03S1
F13-10115
SP MC-002
SP@
CV-403 TAKE UP
TOWER
13-0362-PW-SS3-50
50VB03S1
F13-10466
SP MC-002
SP@
CV-403 TAKE UP
TOWER
13-0727-PW-SS3-50
50VB03S1
F13-10116
SP MC-002
SP@
CV-403 TAKE UP
TOWER
PE16
SS3
110x63
13-1594-PW-SS3-50
50VB03S1
F13-11795
SP MC-002
SP@
GF MILLING
GRID E8
50x25
25VB03S1
F13-11796
SP MC-001
PE16
SS3
110x63
13-1596-PW-SS3-50
50VB03S1
F13-11794
SP MC-002
SP@
MILLING
OPPOSITE F13-SA-401
50x25
25VB03S1
F13-11793
SP MC-001
13-1597-PW-SS3-50
50x25
25VB03S1
F13-11792
SP MC-001
SP@
MILL DECK
NEXT TO F14-SA-407
SP@
L2 CLASSIFICATION
SP MC-001
25VB03S1
F14-10480
50x25
14-0176-PW-SS3-50
SP@
L2 CLASSIFICATION
SP MC-001
25VB03S1
F14-10479
14-2489-PW-SS3-50
50x25
SP@
GRAVITY OVERSIZE
ROCKBOX LEVEL
SP MC-001
25VB03S1
F14-10506
14-2490-PW-SS3-25
SP@
L3 CLASSIFICATION
SP MC-001
25VB03S1
F14-10478
50x25
14-0166-PW-SS3-50
SP@
L4 CLASSIFICATION
SP MC-001
25VB03S1
F14-10481
50x25
14-0177-PW-SS3-50
SP@
MILL DECK
GRID A8
SP MC-001
25VB03S1
F13-11803
50x25
13-1600-PW-S
SP@
F13-CH-452
TOS 377.05
SP MC-001
25VB03S1
F13-10820
50x25
13-1779-PW-SS3-50
SP@
GF OUTSIDE SAG
LUBE ENCLOSURE
SP MC-002
50VB03S1
F13-10818
13-1778-PW-SS3-50
SP MC-001
25VB03S1
F13-10819
50x25
SP@
MILL DECK
GRID C10
SP MC-001
50VB03S1
F13-11804
50x25
13-1599-PW-SS3-50
SP@
GF MILLING
GRID C9
SP MC-002
50VB03S1
F13-11802
13-1598-PW-SS3-50
SP MC-001
25VB03S1
F13-11801
50x25
14-0163-PW-SS3-50
50x25
25VB03S1
F14-10477
SP MC-001
SP@
GRAVITY CLASSIFICATION
TOP LEVEL
14-0175-PW-SS3-50
50x25
25VB03S1
F14-10476
SP MC-001
SP@
GRAVITY CLASSIFICATION
TOP LEVEL
14-0165-PW-SS3-50
50x25
25VB03S1
F14-10475
SP MC-001
SP@
GRAVITY CLASSIFICATION
TOP LEVEL
SS3
PE16
13-0123-PW-PE16-90
MILL FEED END SUMP PUMP
2000-F13-PID-PR-10003
HP PROCESS WATER
13-0031-PW-PE16-225
BALL MILL TROMMEL
2000-F13-PID-PR-10004
HP PROCESS WATER
13-0872-PW-PE16-225
SAG MILL TROMMEL
2000-F13-PID-PR-10003
HP PROCESS WATER
13-0969-PW-PE16-400
PE16
SS2
13-0055-PW-SS2-400
CYCLONE FEED
PUMP SUCTION FLUSH
2000-F13-PID-PR-10002
HP PROCESS WATER
PE16
SS3
13-0050-PW-PE16-280
SAG MILL DISCHARGE SCREEN
2000-F13-PID-PR-10002
HP PROCESS WATER
13-0142-PW-PE16-110
MILL DISCHARGE AREA
DRIVE-IN SUMP MONITOR
2000-F13-PID-PR-10003
HP PROCESS WATER
13-0122-PW-PE16-160
MILL DISCHARGE END SUMP PUMP
2000-F13-PID-PR-10003
HP PROCESS WATER
PE16
SS3
13-0886-PW-SS3-50
50VB03S1
F13-10413
SP MC-002
50x25
25VB03S1
F13-12383
SP MC-001
14-0072-PW-PE16-110
GRAVITY SCREEN OVERSIZE CHUTE
2000-F14-PID-PR-10001
HP PROCESS WATER
14-0179-PW-SS2-300
GRAVITY SCREEN FEED BOX 2
2000-F14-PID-PR-10001
HP PROCESS WATER
14-0132-PW-PE16-225
GRAVITY SCREEN FEED BOX 1
2000-F14-PID-PR-10001
HP PROCESS WATER
PE16
SS3
14-0178-PW-SS3-50
14-0164-PW-SS3-50
50x25
25VB03S1
F14-10472
SP MC-001
SP@
GRAVITY CLASSIFICATION
TOP LEVEL
14-0181-PW-SS3-50
50x25
25VB03S1
F14-10473
SP MC-001
SP@
GRAVITY CLASSIFICATION
TOP LEVEL
14-0981-PW-SS3-50
50x25
25VB03S1
F14-10492
SP MC-001
SP@
GRAVITY CLASSIFICATION
TOP LEVEL
14-1151-PW-SS3-50
50x25
25VB03S1
F14-10474
SP MC-001
SP@
GRAVITY CLASSIFICATION
TOP LEVEL
13-0382-PW-SS2-250
TRASH SCREEN FINAL
COLLECTION BOX
2000-F13-PID-PR-10008
HP PROCESS WATER
13-0075-PW-PE16-110
PE16
SS2
13-0065-PW-SS2-100
TRASH SCREEN 1
2000-F13-PID-PR-10007
HP PROCESS WATER
13-0076-PW-PE16-110
PE16
SS2
13-0069-PW-SS2-100
TRASH SCREEN 2
2000-F13-PID-PR-10007
HP PROCESS WATER
13-0074-PW-PE16-110
PE16
SS2
13-0170-PW-SS2-100
TRASH SCREEN 4
2000-F13-PID-PR-10008
HP PROCESS WATER
13-0087-PW-PE16-110
PE16
SS2
13-0073-PW-SS2-100
TRASH SCREEN 3
2000-F13-PID-PR-10008
HP PROCESS WATER
SS2
PE16
450x315
13-0062-PW-PE16-450
13-1276-PW-PE16-90
TRASH DEWATERING
SCREEN SPRAYS
2000-F13-PID-PR-10007
HP PROCESS WATER
16-0247-PW-PE16-315
ROUGHER FLOTATION CELL 1
2000-F16-PID-PR-10001
HP PROCESS WATER

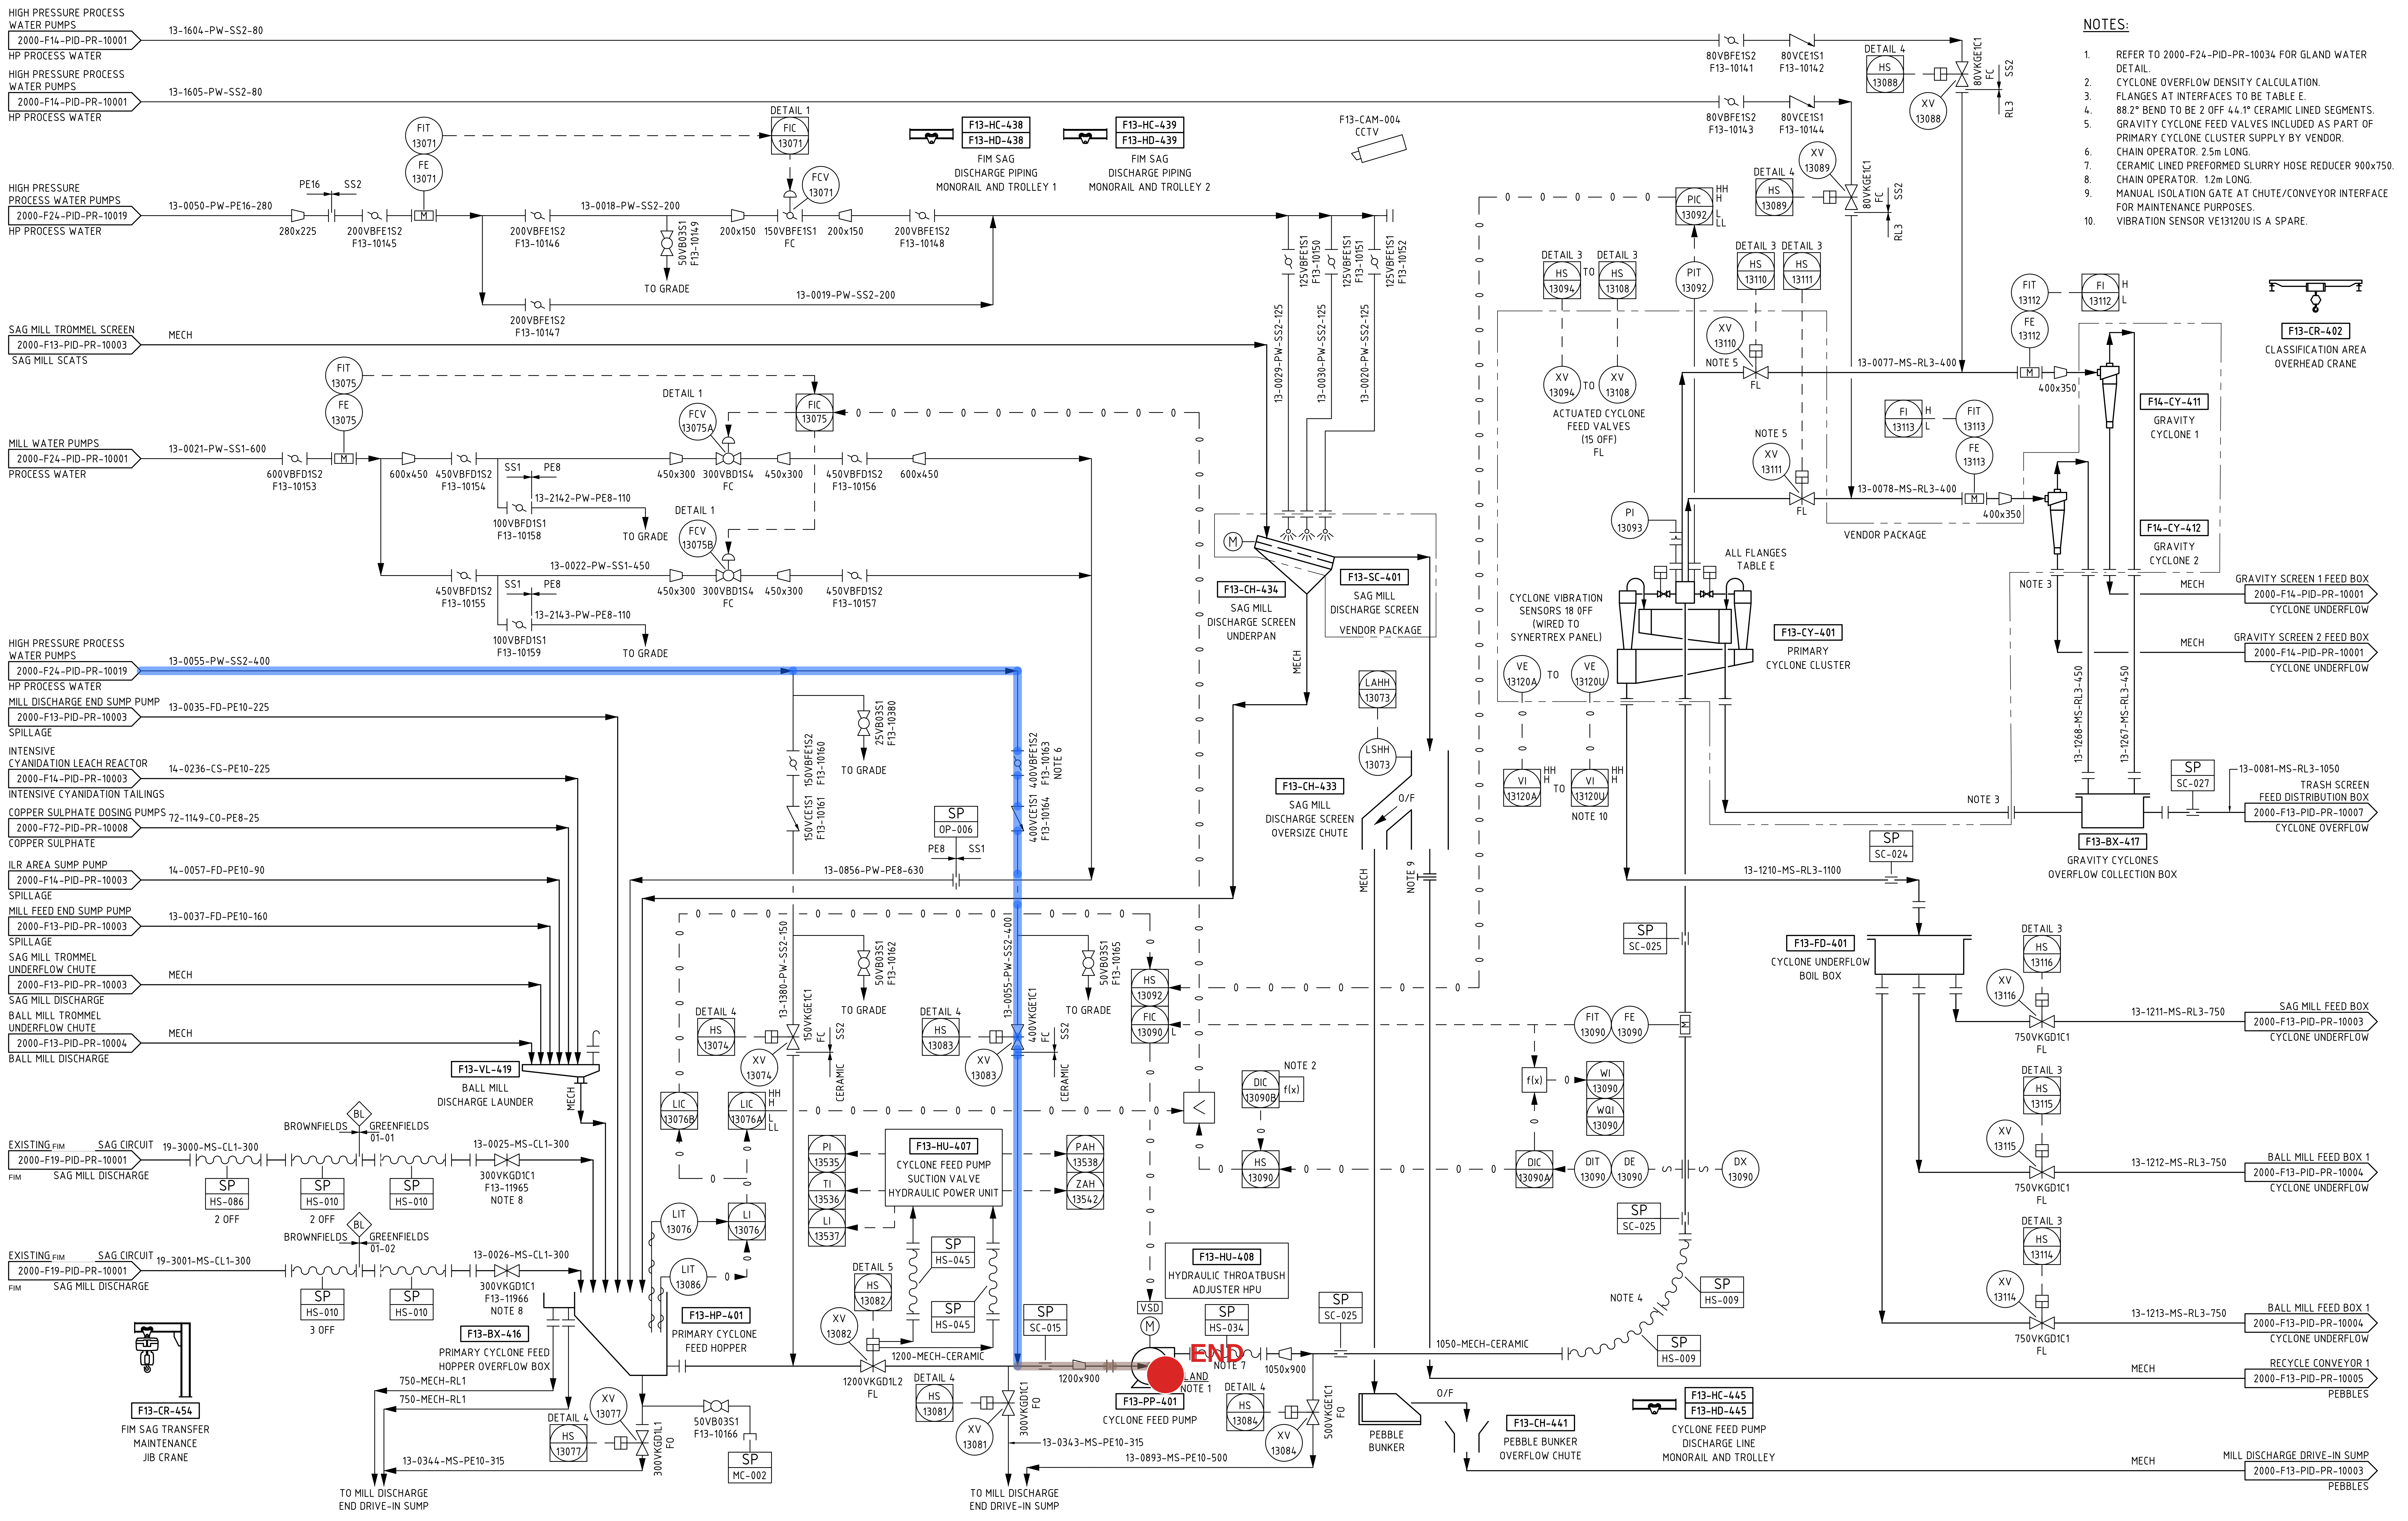

NOTES:

1. REFER TO 2000-F24-PID-PR-10034 FOR GLAND WATER DETAIL.
2. CYCLONE OVERFLOW DENSITY CALCULATION.
3. FLANGES AT INTERFACES TO BE TABLE E.
4. 88.2° BEND TO BE 2 OFF 44.1° CERAMIC LINED SEGMENTS.
5. GRAVITY CYCLONE FEED VALVES INCLUDED AS PART OF PRIMARY CYCLONE CLUSTER SUPPLY BY VENDOR.
6. CHAIN OPERATOR. 2.5m LONG.
7. CERAMIC LINED PREFORMED SLURRY HOSE REDUCER 900x750.
8. CHAIN OPERATOR. 1.2m LONG.
9. MANUAL ISOLATION GATE AT CHUTE/CONVEYOR INTERFACE FOR MAINTENANCE PURPOSES.
10. VIBRATION SENSOR VE13120U IS A SPARE.